



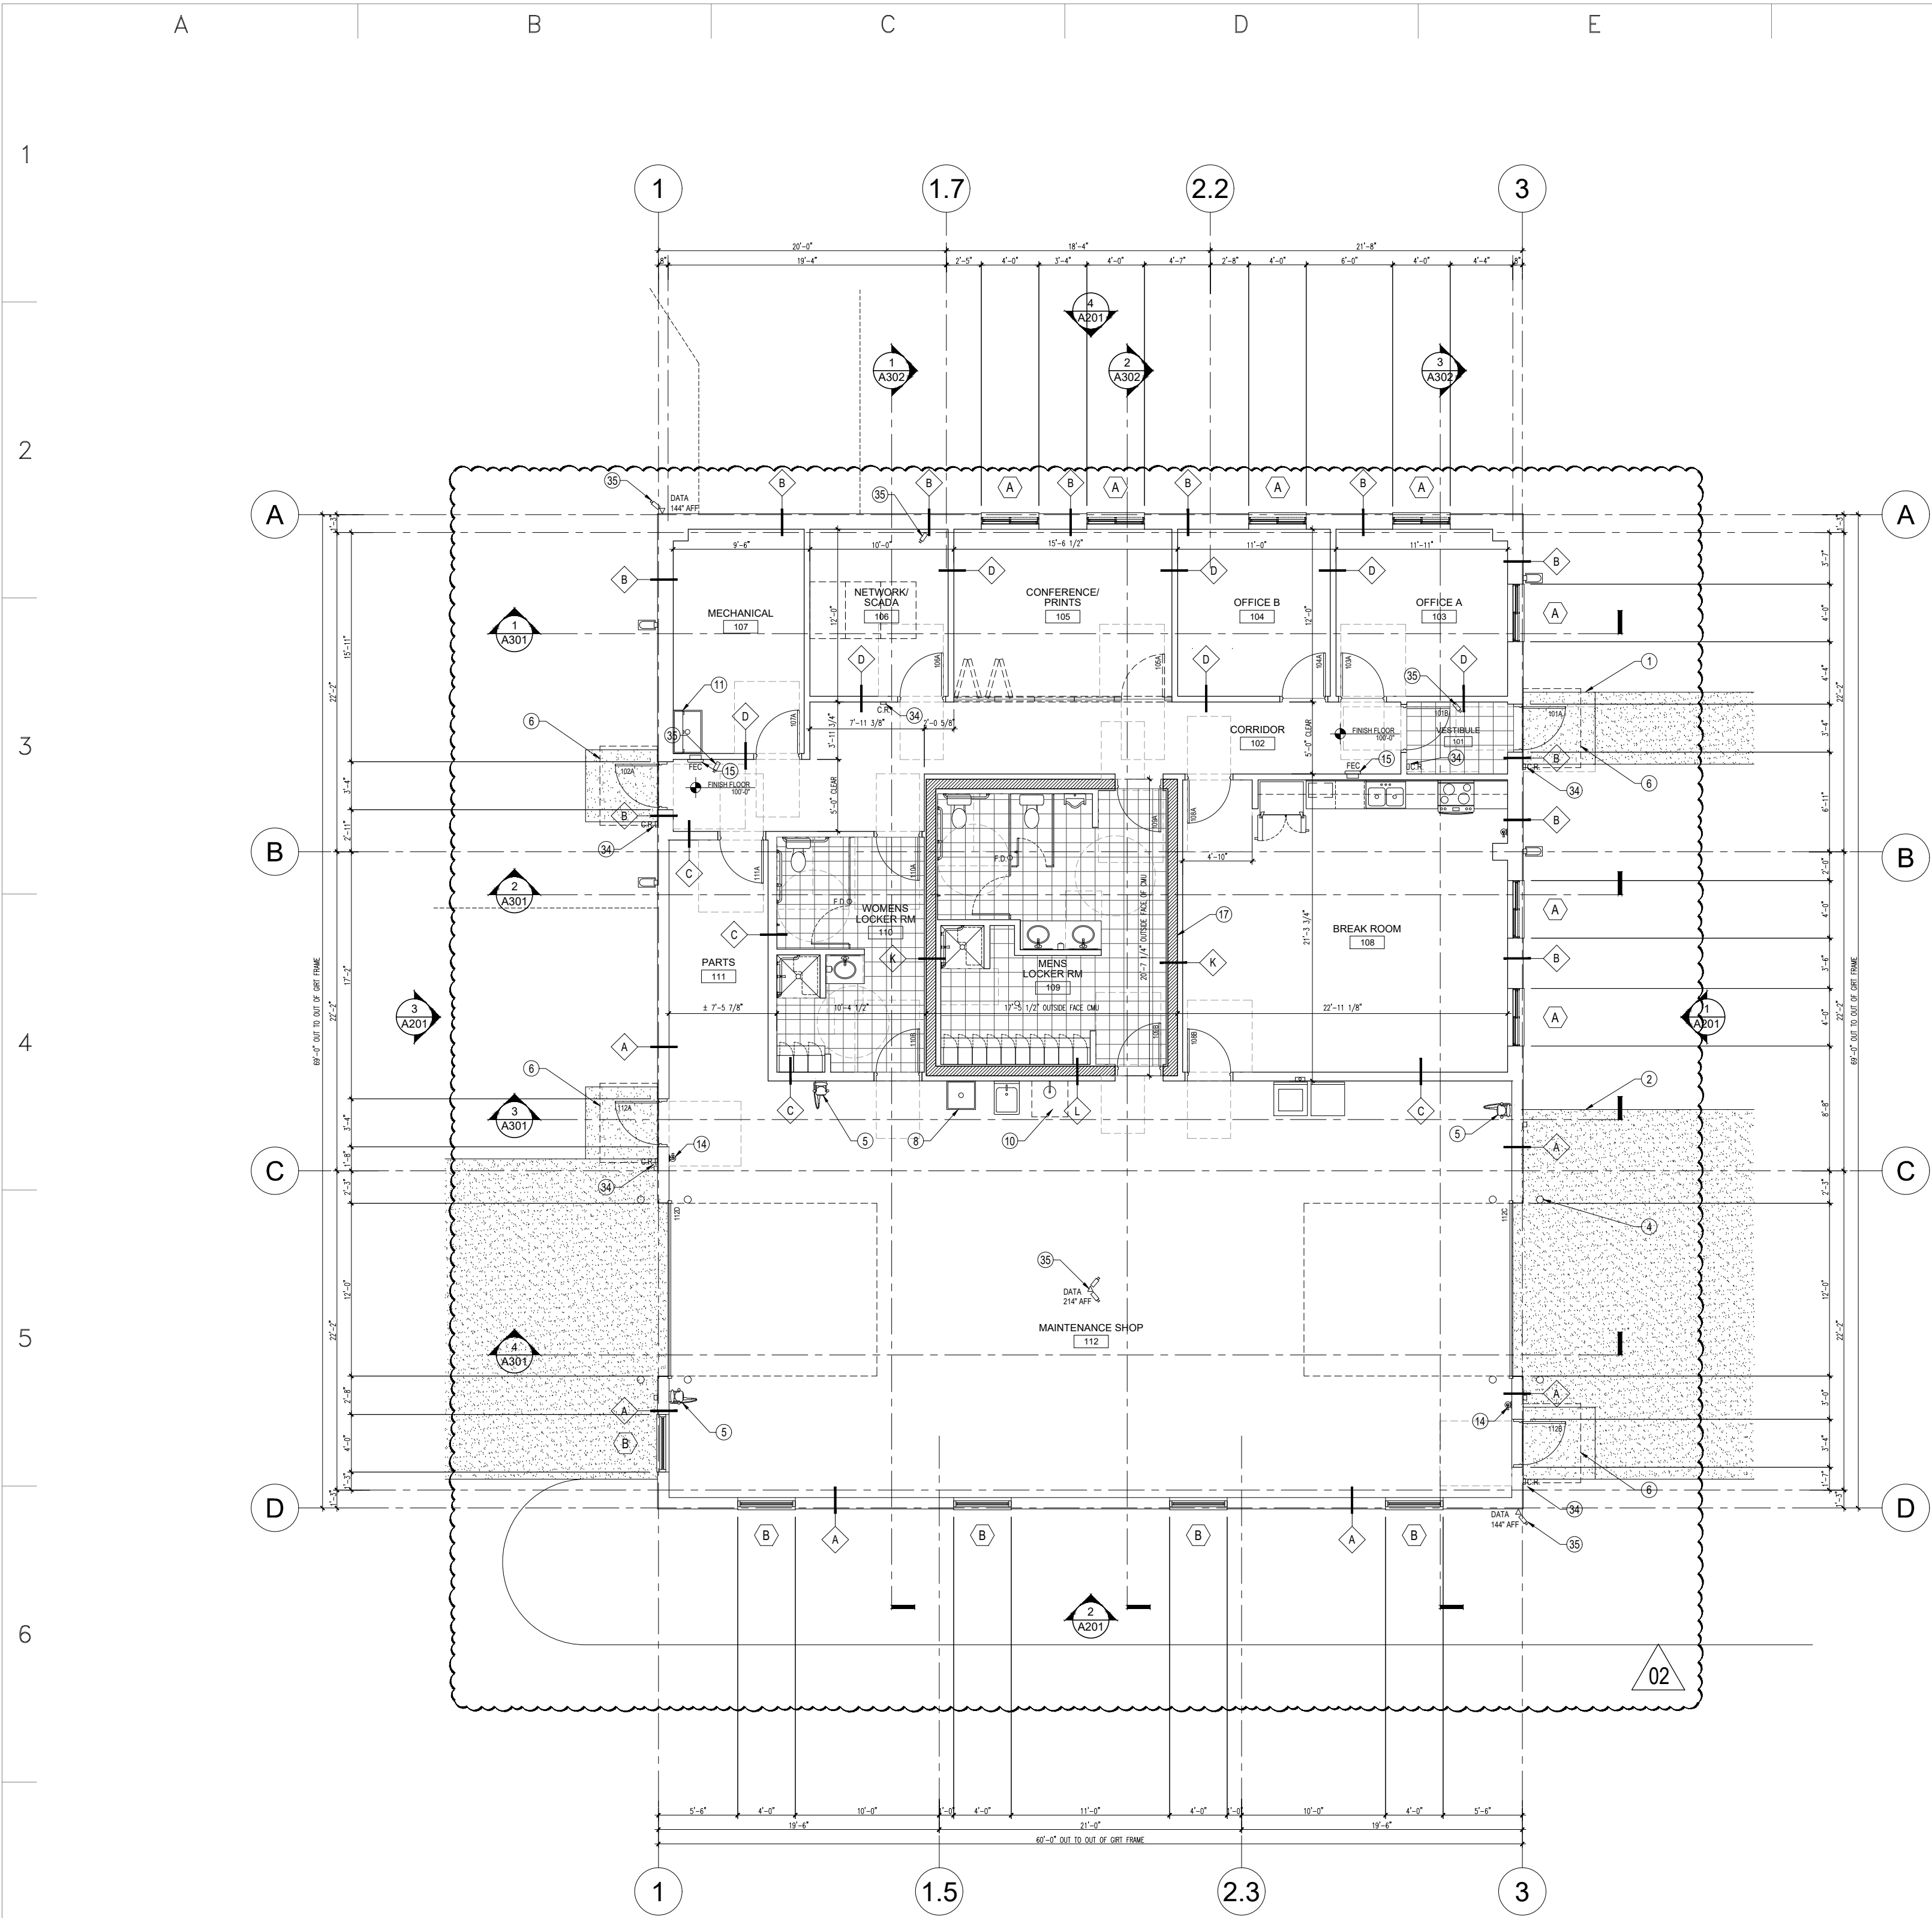

1 FLOOR PLAN
SCALE: 1/8" = 1'-0"

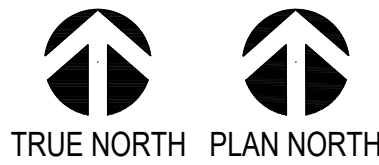

PLAN KEY NOTES

- 5'x5'x5" CONCRETE STOOP w/ 4" THICK CONCRETE SIDEWALKS. REFER STRUCTURAL
- 6" REINFORCED CONCRETE APRON w/ 6" BOLLARDS
- TRENCH DRAIN
- 6" STEEL BOLLARD.
- WALL MOUNT EV CHANGING STATION
- 5'-6"x4'-0" ICE SHIELD CANOPY
- 199,900 BTU TANKLESS WATER HEATER w/ RE-CIRCULATION PUMP.
- 24"x24" UTILITY SINK. INSTALL FRP BOARD ON 3/4" EXTERIOR GRADE PLYWOOD 4'-0" WIDE x 8'-0" HIGH BEHIND SINK.
- WATER COOLER
- EMERGENCY EYE WASH STATION
- 24"x36"x10" MOP SINK, SEAL ALL EDGES
- FREEZE PROOF HOSE BIB, FOUR EXTERIOR AND ONE INTERIOR
- 12'-0"x5'-0"x6" REINFORCED CONCRETE APRON w/ TWO 6" DIA. CONCRETE FILED BOLLARDS
- WALL MOUNTED 3A-40B-C FIRE EXTINGUISHER
- SEMI RECESSED FIRE EXTINGUISHER CABINET w/ 3A-40B-C FIRE EXTINGUISHER
- NOT USED
- SHELTER ROOM w/ 8" CMU WALLS AND 10" CONCRETE CEILING SLAB. REFER STRUCTURAL
- 2" DIA. SLEEVE FOR OPTICAL FIBER CABLE AT 6" O.C. THRU FOUNDATION GRADE BEAM.
- 4" DIA. SLEEVES FOR PHONE AND CABLE AT 6" O.C. THRU FOUNDATION GRADE BEAM AT 30" TO TOP OF SLEEVE
- 4" DIA. SLEEVE FOR GAS LINE AT 30" TO TOP OF SLEEVE.
- 6" DIA. SLEEVE FOR SANITARY SEWER LINE AT TOP OF FOOTING
- 6" DIA. SLEEVE FOR HOLDING TANK AT 30" TO TOP OF SLEEVE
- CORNER GUARDS (4'-0" HIGH, CLEAR PLASTIC)
- 4" DIA. SLEEVE FOR POWER AT 6" O.C. THRU FOUNDATION WALL AT 30" TO TOP OF SLEEVE
- WATER LINE INSTALLED UNDER FOOTING AT 8'-0" BELOW GRADE ELEVATION.
- 4" DIA. SLEEVE FOR CAMERAS AT 6" O.C. THRU FOUNDATION WALL AT 30" TO TOP OF SLEEVE
- 4" DIA. FOR POWER TO MAIN GATE AT 6" O.C. THRU FOUNDATION WALL 30" TO TOP OF SLEEVE.
- 2" DIA. SLEEVE THRU FOUNDATION WALL
- 2" DIA CONDUIT BETWEEN ROOM
- EXTEND TWO CONDUIT TO SCADA ROOM AND ONE CONDUIT TO IT ROOM
- ACCESSIBLE HI-LO DRINKING FOUNTAIN WITH BOTTLE FILLER - "ELKAY EAZY H20"
- GENERATOR ON CONCRETE PAD, REFER ELECTRICAL
- CONDENSER UNITS ON 5'x5'x4" CONCRETE PADS
- CARD READER CONTROLLED ACCESS
- SECURITY CAMERA, COORDINATE WITH OWNER

GENERAL FLOOR PLAN NOTES

- NOTE: THESE GENERAL NOTES APPLY TO ALL ARCHITECTURAL FLOOR PLANS
- ALL DIMENSIONS ARE FROM FINISHED WALL TO FINISHED WALL UNLESS NOTED OTHERWISE.
 - REFER TO THE MECHANICAL, ELECTRICAL AND PLUMBING DRAWINGS FOR ADDITIONAL NOTES AND WORK THAT MAY NOT BE INDICATED ON THIS DRAWING.
 - ALL EQUIPMENT, FINISHES AND TOILET ACCESSORIES TO BE INSTALLED ARE TO COMPLY WITH ANSI A117.1, AMERICAN WITH DISABILITIES ACT AND OTHER SPECIFIC STANDARDS, CODES AND REGULATIONS ESTABLISHED BY LOCAL AUTHORITIES HAVING JURISDICTION.
 - NOT USED
 - VERIFY ALL DIMENSIONS AND CLEARANCES.
 - ALL MASONRY DIMENSIONS ARE SHOWN AS NOMINAL (±3/8"), UNLESS NOTED OTHERWISE.
 - DO NOT SCALE OFF PLANS. CONTACT ARCHITECT WITH DIMENSION QUESTIONS.
 - EQUIPMENT ROOMS ARE DESIGNED TO BE USED FOR STORAGE OF EQUIPMENT AND ARE NOT TO BE USED FOR STORAGE OF ANY COMBUSTIBLE MATERIALS.
 - GENERAL CONTRACTOR TO COORDINATE CONSTRUCTION PHASING WITH OWNER.
 - THE GENERAL CONTRACTOR IS RESPONSIBLE TO PROVIDE AND INSTALL ALL BLOCKING AND GROUNDS AS REQUIRED FOR THE INSTALLATION OF MILLWORK AND ANY HANGING OBJECTS AS REQUIRED.
 - DOORS WITH WALL STOP TO BE 4" FROM WALL TYPICAL UNO.
 - THE CONTRACTOR SHALL TAKE OUT ALL NECESSARY PERMITS, INSURANCE, LICENSES AND CERTIFICATES AND PAY ALL FEES CONNECTED THEREWITH.
 - THE CONTRACTOR AT ALL TIMES SHALL KEEP THE PREMISES FREE FROM WASTE MATERIALS AND RUBBISH CAUSED BY THE WORK.
 - ALL DOORS AND HARDWARE SHALL BE IN COMPLIANCE WITH APPLICABLE ACCESSIBILITY CODES AND ORDINANCES. ALL WORK TO BE DONE IN COMPLIANCE WITH THE LATEST LOCAL AND STATE BUILDING CODES AND ORDINANCES.
 - PROVIDE 5/8" CEMENT BOARD IN LIEU OF GYPSUM BOARD AT ALL TILE AND WET WALLS.
 - VERIFY ALL SLEEVE LOCATIONS THROUGH FOUNDATION WALL AND ALL UTILITY LOCATIONS WITH MEP AND CIVIL DESIGN.
 - PROVIDE RIGID INSULATION FLASHED TO METAL BUILDING AND DOWN TO FOOTING.
 - VERIFY CODE REQUIREMENTS FOR FIRE EXTINGUISHER.

ISSUED FOR CONSTRUCTION

KUBIER
ARCHITECTURE PLLC
3241 MARINERS DRIVE
PENSACOLA, FLORIDA 32526
(405).226.4619

REVISION						REVISION						REFERENCE DRAWINGS			STATE OF NEW MEXICO				CUNNINGHAM 1 SOLAR PROJECT				DWG NO	
NO	REVISION	ZONE	DATE	BY	CHK	ENG	NO	REVISION	ZONE	DATE	BY	CHK	ENG	DWG. NO.	MANUFACTURER	DESCRIPTION	PUBLIC SERVICE COMPANY OF NEW MEXICO		O&M BUILDING		A103 - FLOOR PLAN		DCSS101-SIMBS301001	
0	ISSUED FOR CONSTRUCTION	X-X	07.30.2025	FK	FK	XXX											FRANCIS KUBIER		NO. 6924		DATE: 07.30.2025		DATE: 00-00-00	
01	DELETED HOLDING TANK	X-X	08.21.2025	FK	FK	XXX											REGISTERED ARCHITECT		Xcel Energy		DATE: 00-00-00		DATE: 00-00-00	
2	FIRE RATED DELETED	X-X	05.03.2026	FK	FK	XXX											APVD: DR		CUNNINGHAM 1 SOLAR FARM		DATE: 00-00-00		DATE: 00-00-00	
																	07/30/2025		LEA COUNTY, NM		PROJ. NO: 0002117001		SCALE: NONE	
																	DWN: FK		ENERGY SUPPLY		SHEET NO		10	
																	DATE: 07.30.2025		ENGINEERING & CONSTRUCTION		REV		02	