


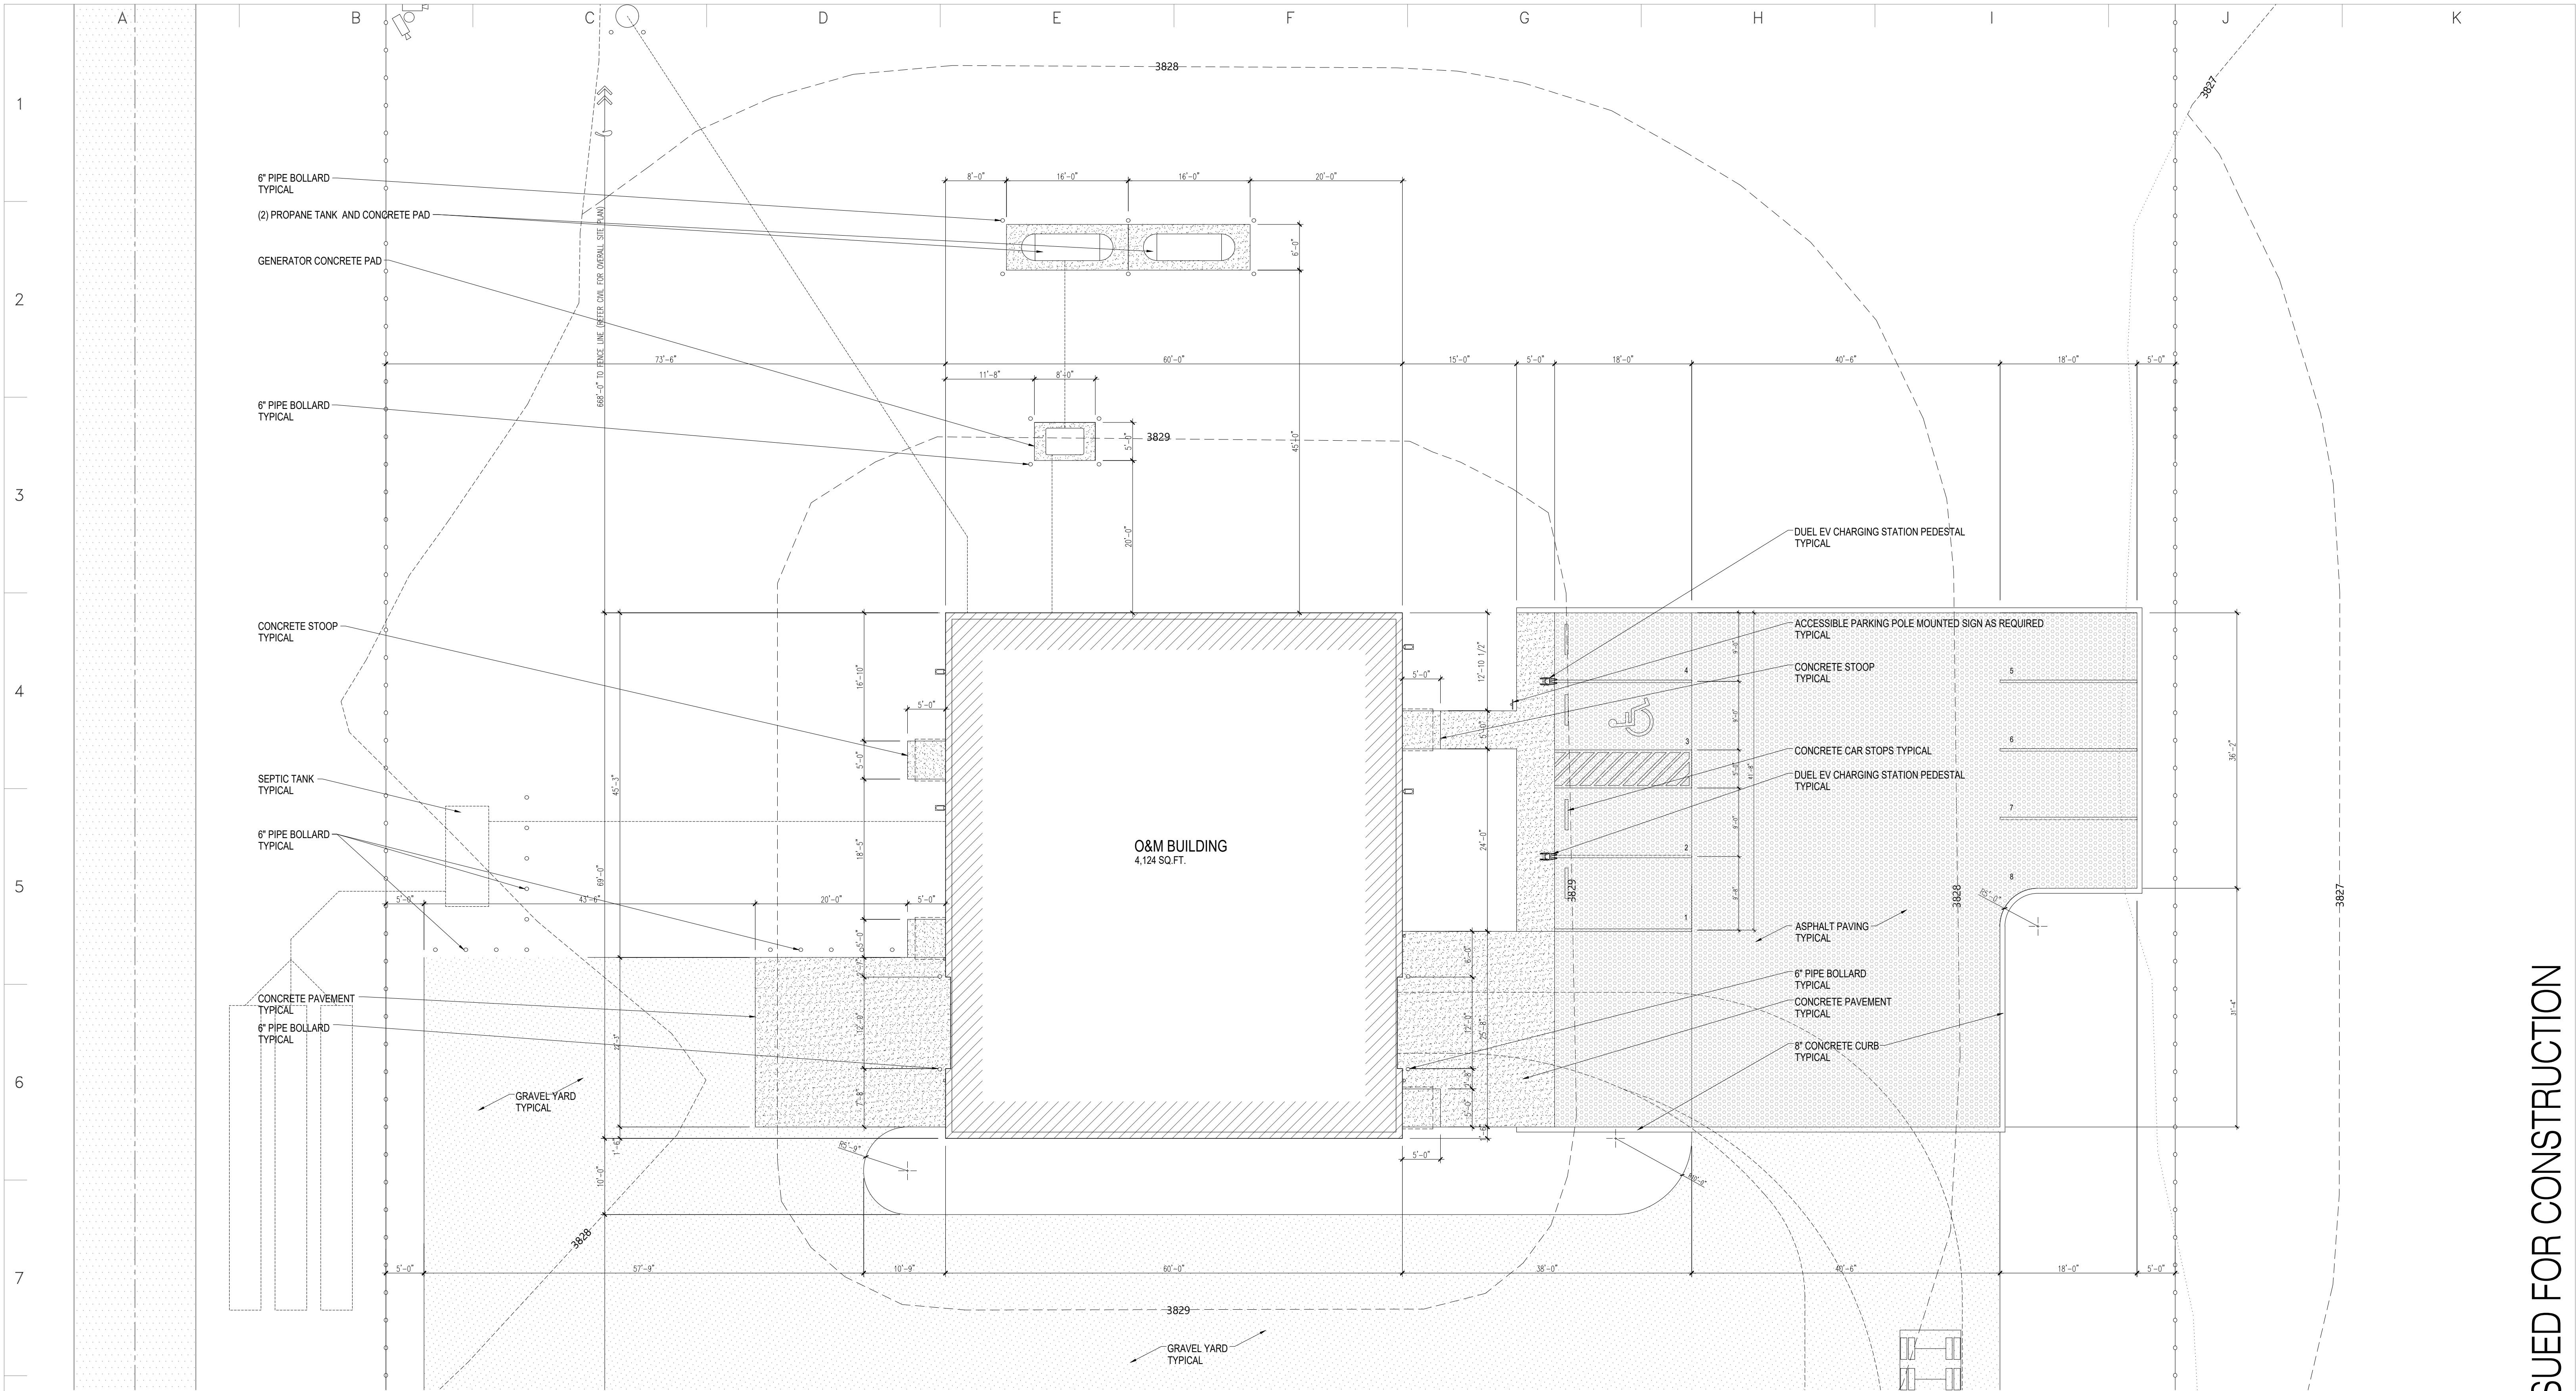

1 ENLARGED SITE PLAN
SCALE: 1" = 10'-0"

TRUE NORTH PLAN NORTH

ISSUED FOR CONSTRUCTION

ka KUBIER
ARCHITECTURE PLLC
3241 MARINERS DRIVE
PENSACOLA, FLORIDA 32526
(405).226.4619

REVISION						REVISION						REFERENCE DRAWINGS			STATE OF NEW MEXICO FRANCIS KUBIER NO. 6924 REGISTERED ARCHITECT 01/30/2025 Xcel Energy® Public Service Company of New Mexico CUNNINGHAM 1 SOLAR FARM LEA COUNTY, NM DWN: FK DATE: 07.30.2025 CHK: FK DATE: 07.30.2025 ENG: N/A DATE: 00-00-00 CHK: DATE: 00-00-00 PM: DR DATE: 00-00-00 PROJ. NO: 0002117001 APVD: DR DATE: 00-00-00 SCALE: NONE CUNNINGHAM 1 SOLAR PROJECT O&M BUILDING A102 – WNLARGED SITE PLAN ENERGY SUPPLY ENGINEERING & CONSTRUCTION DWG NO DCSS101-SIMBS301001 SHEET NO 09 REV 01			
NO	ISSUED FOR CONSTRUCTION	ZONE	DATE	BY	CHK	ENG	NO	ISSUED FOR CONSTRUCTION	ZONE	DATE	BY	CHK	ENG	DWG NO.				
0	ISSUED FOR CONSTRUCTION	X-X	07.30.2025	FK	FK	XXX												
01	REVISED ADA PARKING SIGN	X-X	08.21.2025	FK	FK	XXX												
						</												